ARCHICAD EDUCATION VERSION

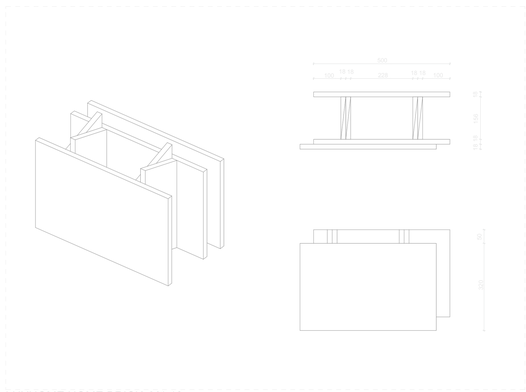

LUXHOME HOME BRICK M1:10

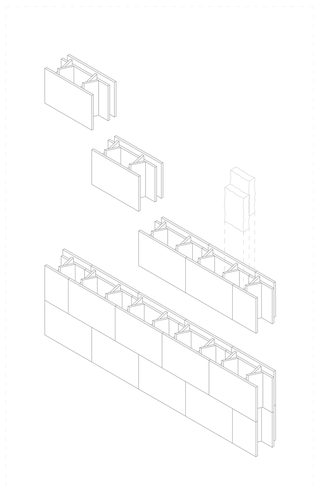

AXONOMETRIE HOME BRICK SYSTEM M1:20

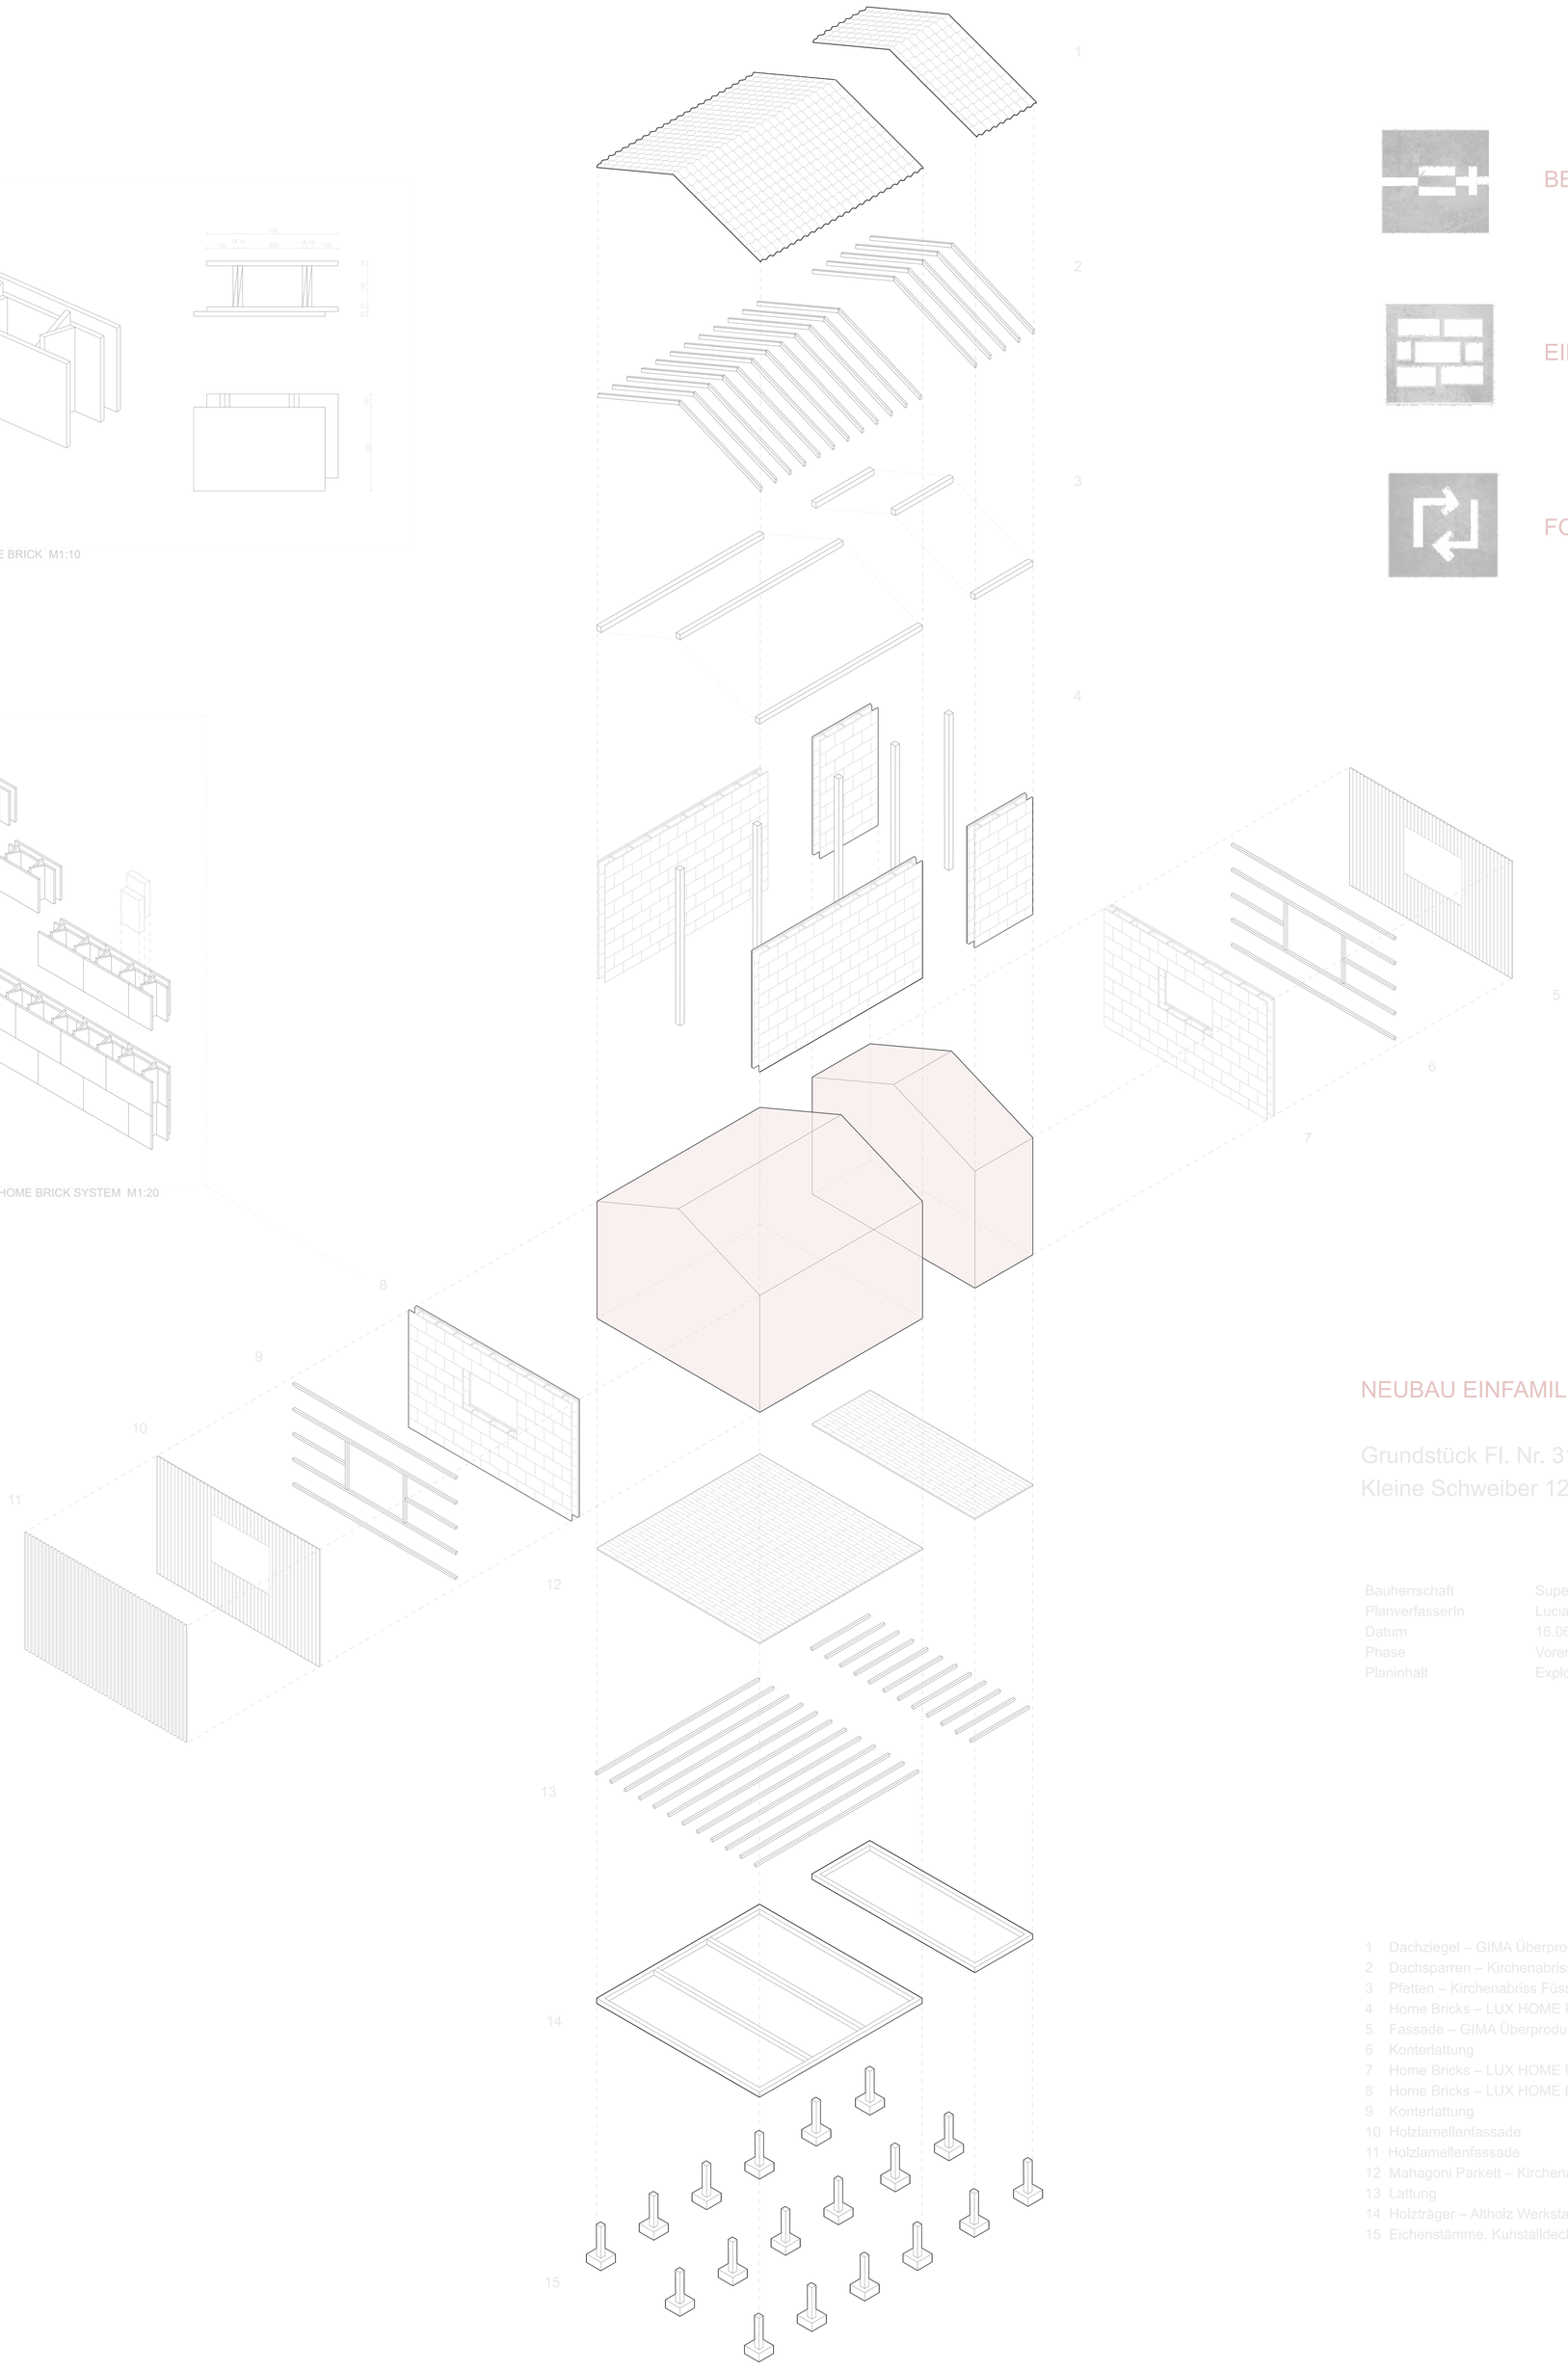

BESCHEIDENHEIT

EINFACHES BAUEN

FORM ↔ VORHANDENHEIT

NEUBAU EINFAMILIENHAUS AGUIRRE

Grundstück Fl. Nr. 314/42.
Kleine Schweiber 12, 87660 Irsee

Bauherrschaft	Supertecture 2
PlanverfasserIn	Luciana Rudolph
Datum	16.06.2024
Phase	Vorentwurf
Planinhalt	Explosionszeichnung Rohbau

1 Dachziegel – GIMA Überproduktion
2 Dachsparren – Kirchenabriss Füssen
3 Pfetten – Kirchenabriss Füssen
4 Home Bricks – LUX HOME Patent, GIMA B-Ware, BAUFRITZ Verschnitt
5 Fassade – GIMA Überproduktion
6 Konterlattung
7 Home Bricks – LUX HOME Patent, GIMA B-Ware, BAUFRITZ Verschnitt
8 Home Bricks – LUX HOME Patent, GIMA B-Ware, BAUFRITZ Verschnitt
9 Konterlattung
10 Holzlamellenfassade
11 Holzlamellenfassade
12 Mahagoni Parkett – Kirchenabriss Füssen
13 Lattung
14 Holzträger – Altholz Werkstatt Riedle + Bader
15 Eichenstämme, Kuhstalldecke – Abriss Kuhstall